

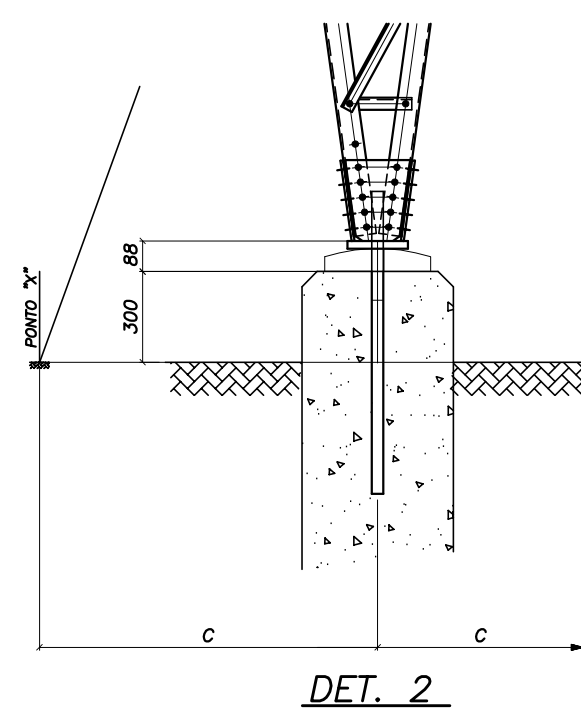
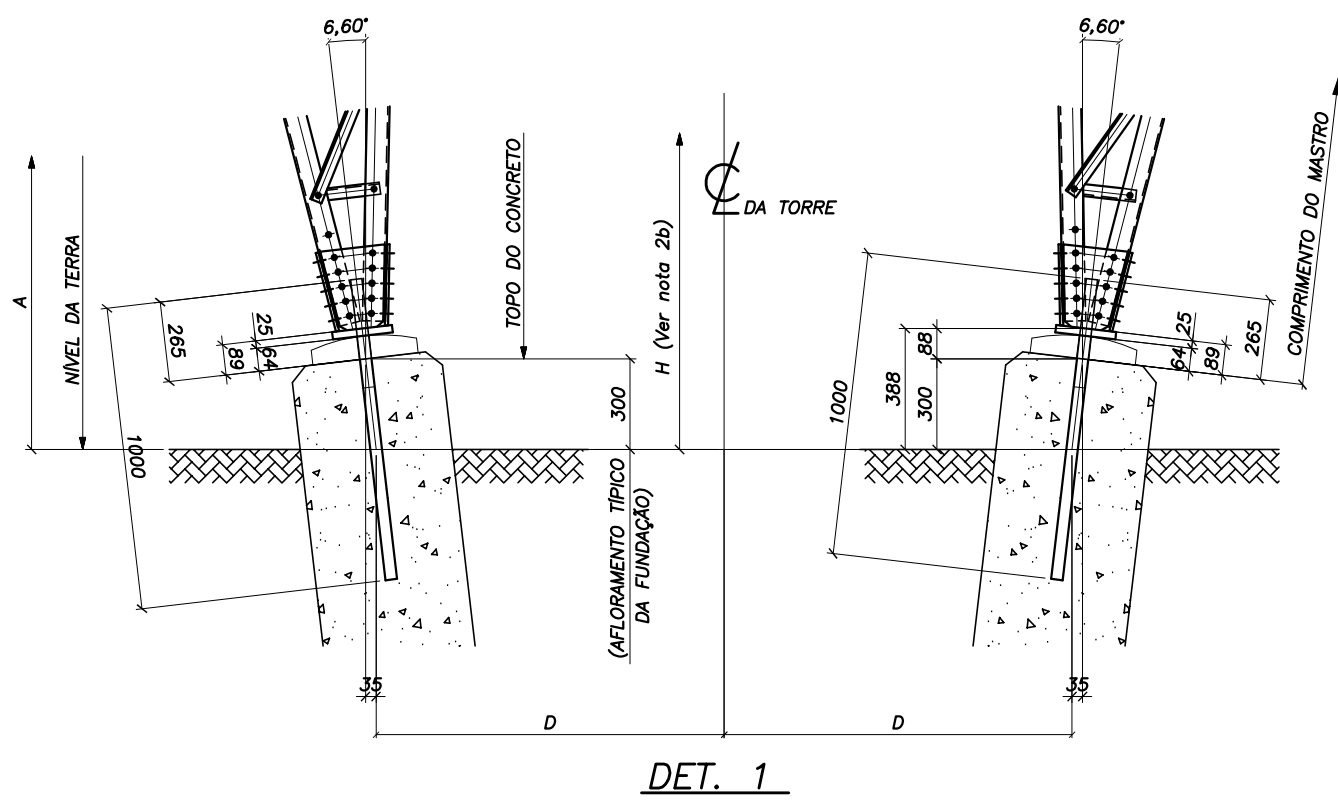
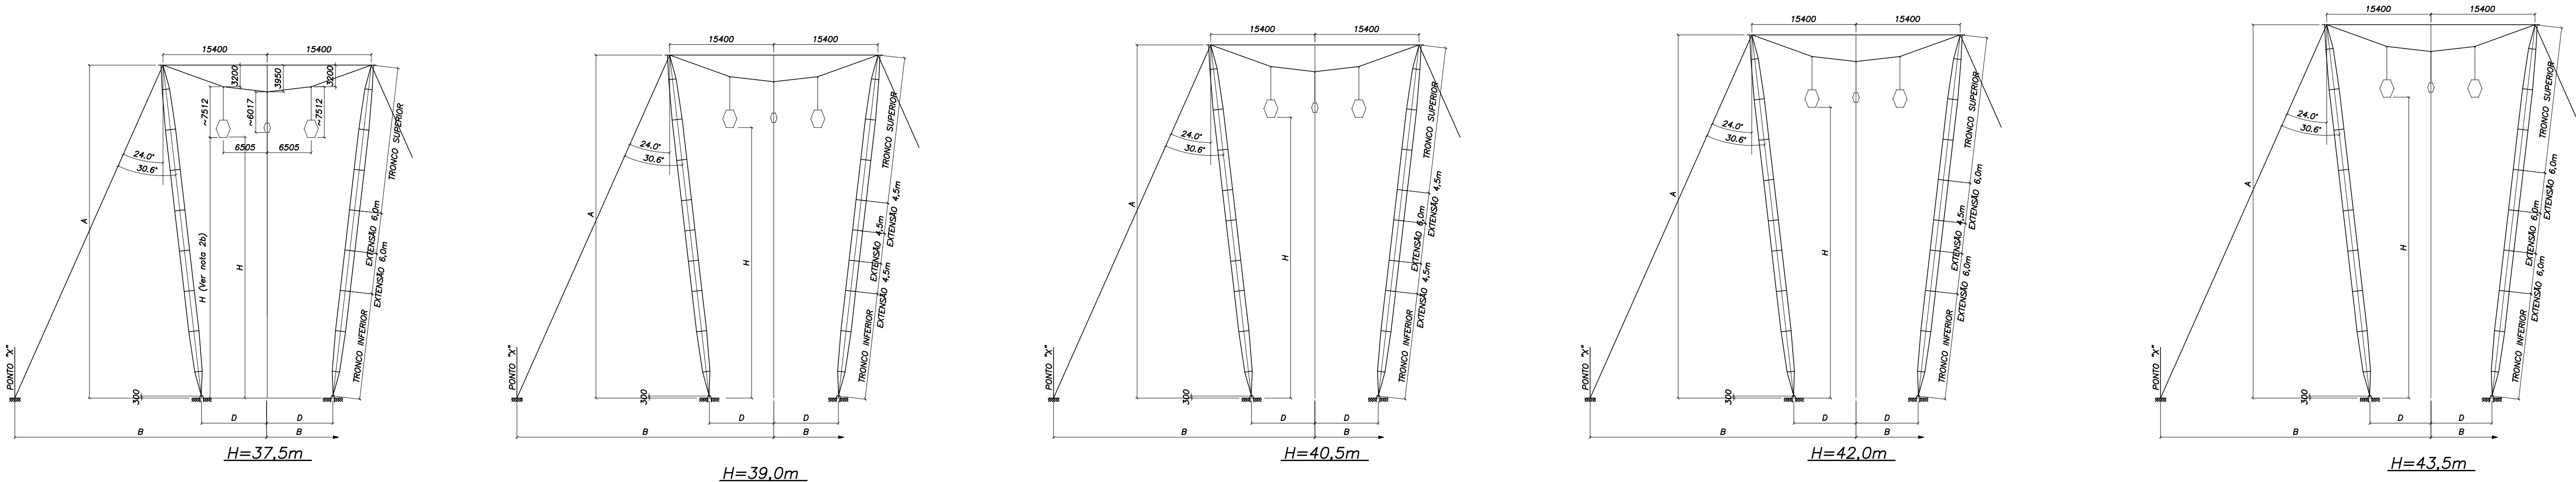


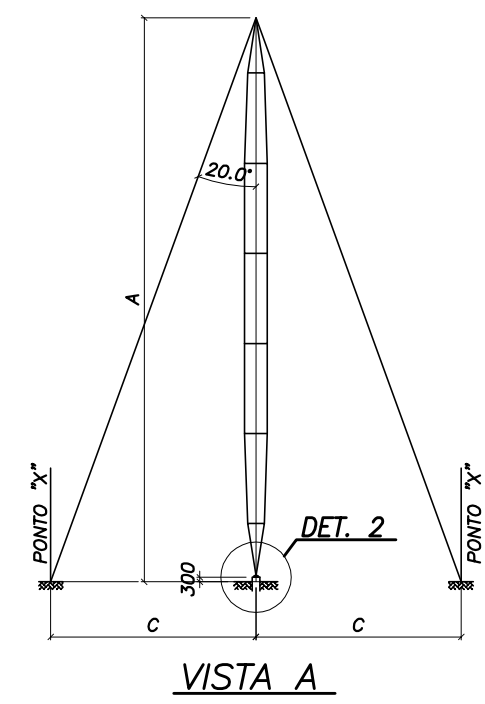

FORMAÇÃO DAS ALTURAS (1 MASTRO)						
TORRES		H=37,5m	H=39,0m	H=40,5m	H=42,0m	H=43,5m
QUANTIDADES	COMPONENTES					
	TRONCO SUPERIOR	1	1	1	1	1
	TRONCO INTERIOR	1	1	1	1	1
	EXTENSÃO 4,5m	—	3	2	1	—
	EXTENSÃO 6,0m	2	—	1	2	3

LOCAÇÃO DOS ESTAIS e MASTROS						
TORRES		H=37,5m	H=39,0m	H=40,5m	H=42,0m	H=43,5m
DIMENSÕES						
A		49224	50714	52204	53694	55184
B		37316	37979	38643	39306	39969
C		17916	18458	19001	19543	20085
D		9705	9532	9360	9187	9015
H		38058	39539	41019	42500	43980
COMPRIMENTO TEÓRICO DE 1 ESTAI (L)		56783	58502	60220	61939	63658

NOTAS: 1— AS DIMENSÕES A, B, C, D, H e L DA TABELA ACIMA FORAM ESTABELECIDAS PARA TERRENO PERFEITAMENTE NIVELADO. PARA TERRENOS COM DESNÍVEIS, OS ESTAIS DEVERÃO SER LOCADOS OBEDECENDO-SE AOS ÂNGULOS DE INCLINAÇÃO INDICADOS NOS ESQUEMAS ACIMA (24°, NO PLANO TRANSVERSAL, e 20°, NO PLANO LONGITUDINAL).
2— AS QUANTIDADES INDICADAS DE COMPONENTES SÃO PARA 1 MASTRO.




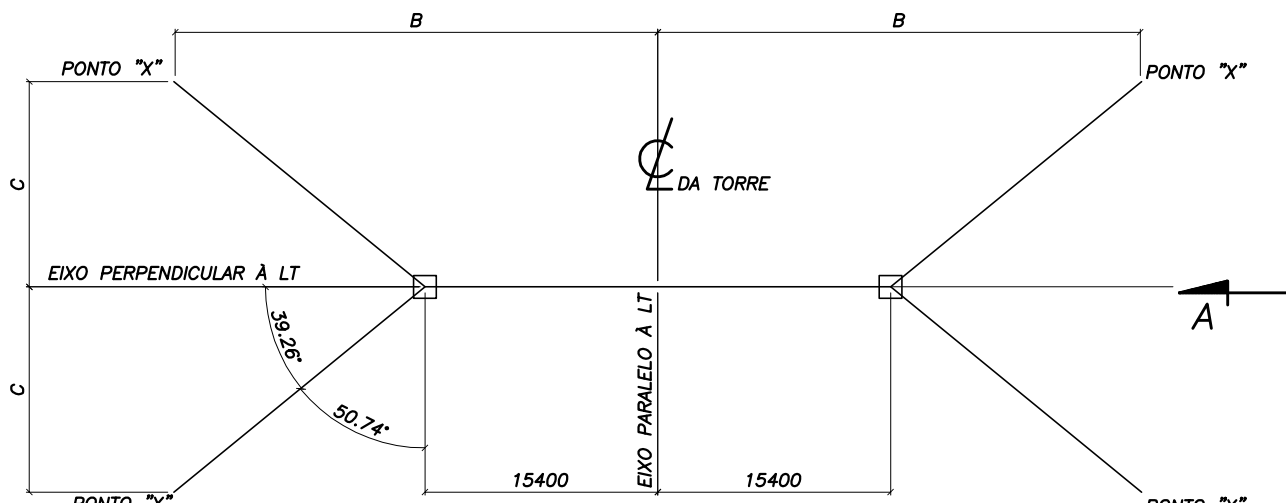


1)REFERÊNCIAS:

- 1a) ESPECIFICAÇÕES, NOTAS GERAIS e RELAÇÃO DE DESENHOS 482.03-D11001
1b) ESQUEMAS P/ APOIO DOS MASTROS, P/ ESTAIS
e P/ CABOS DE INTERLIGAÇÃO DOS MASTROS
e DE SUSPENSÃO DAS FASES 482.03-D11005

2)NOTAS P/ SILHUETAS COM FORMAÇÃO DAS ALTURAS:

- 2a) AS COTAS APRESENTADAS PARA O TOPO DOS MASTROS E PARA OS PONTOS DE FIXAÇÃO DAS CADEIAS DE SUSPENSÃO DAS FASES CORRESPONDEM A VALORES TEÓRICOS NOMINAIS, OBTIDOS A PARTIR DOS COMPRIMENTOS INDEFORMADOS DOS CABOS DE INTERLIGAÇÃO DOS MASTROS E DE SUSPENSÃO DAS FASES.
2b) A DIMENSÃO H CORRESPONDE À DISTÂNCIA ENTRE CONDUTORES INFERIORES DAS FASES LATERAIS E A LINHA DE TERRA NA CONDIÇÃO EDS DE CARGA G1 (VER CÁLCULO ESTRUTURAL ENGETOWER N° 482.03-C11001).
2c) OS ESQUEMAS MOSTRADOS NO DESENHO 482.03-D11005 ESCLARECEM COM MAIS DETALHES AS REFERÊNCIAS PARA AS COTAS A, B, C, D e H.

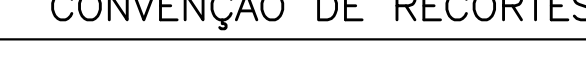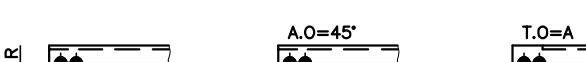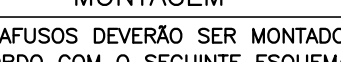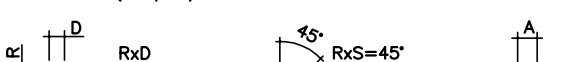CONVENÇÃO DE RECORTES			PARAFUSOS										
			Símbolo	Ø Parafuso	Ø Furo	K	R	COMPRIMENTOS		TORQUE (kgf.m)		MONTAGEM	
				M12	13,5	20	22	A=30	H=65	Ø	Min.	Max.	OS PARAFUSOS DEVERÃO SER MONTADOS DE ACORDO COM O SEGUINTE ESQUEMA: 
				M16	17,5	25	28	B=35	I=70	M12	3,0	4,5	
				M20	21,5	30	30	C=40	J=75	M16	7,5	11,5	
				M24	25,5	40	34	D=45	K=80	M20	13,0	22,0	
				Parafuso Degrau Ø15,9	17,5	—	70	E=50	L=85	M24	20,0	39,0	
